



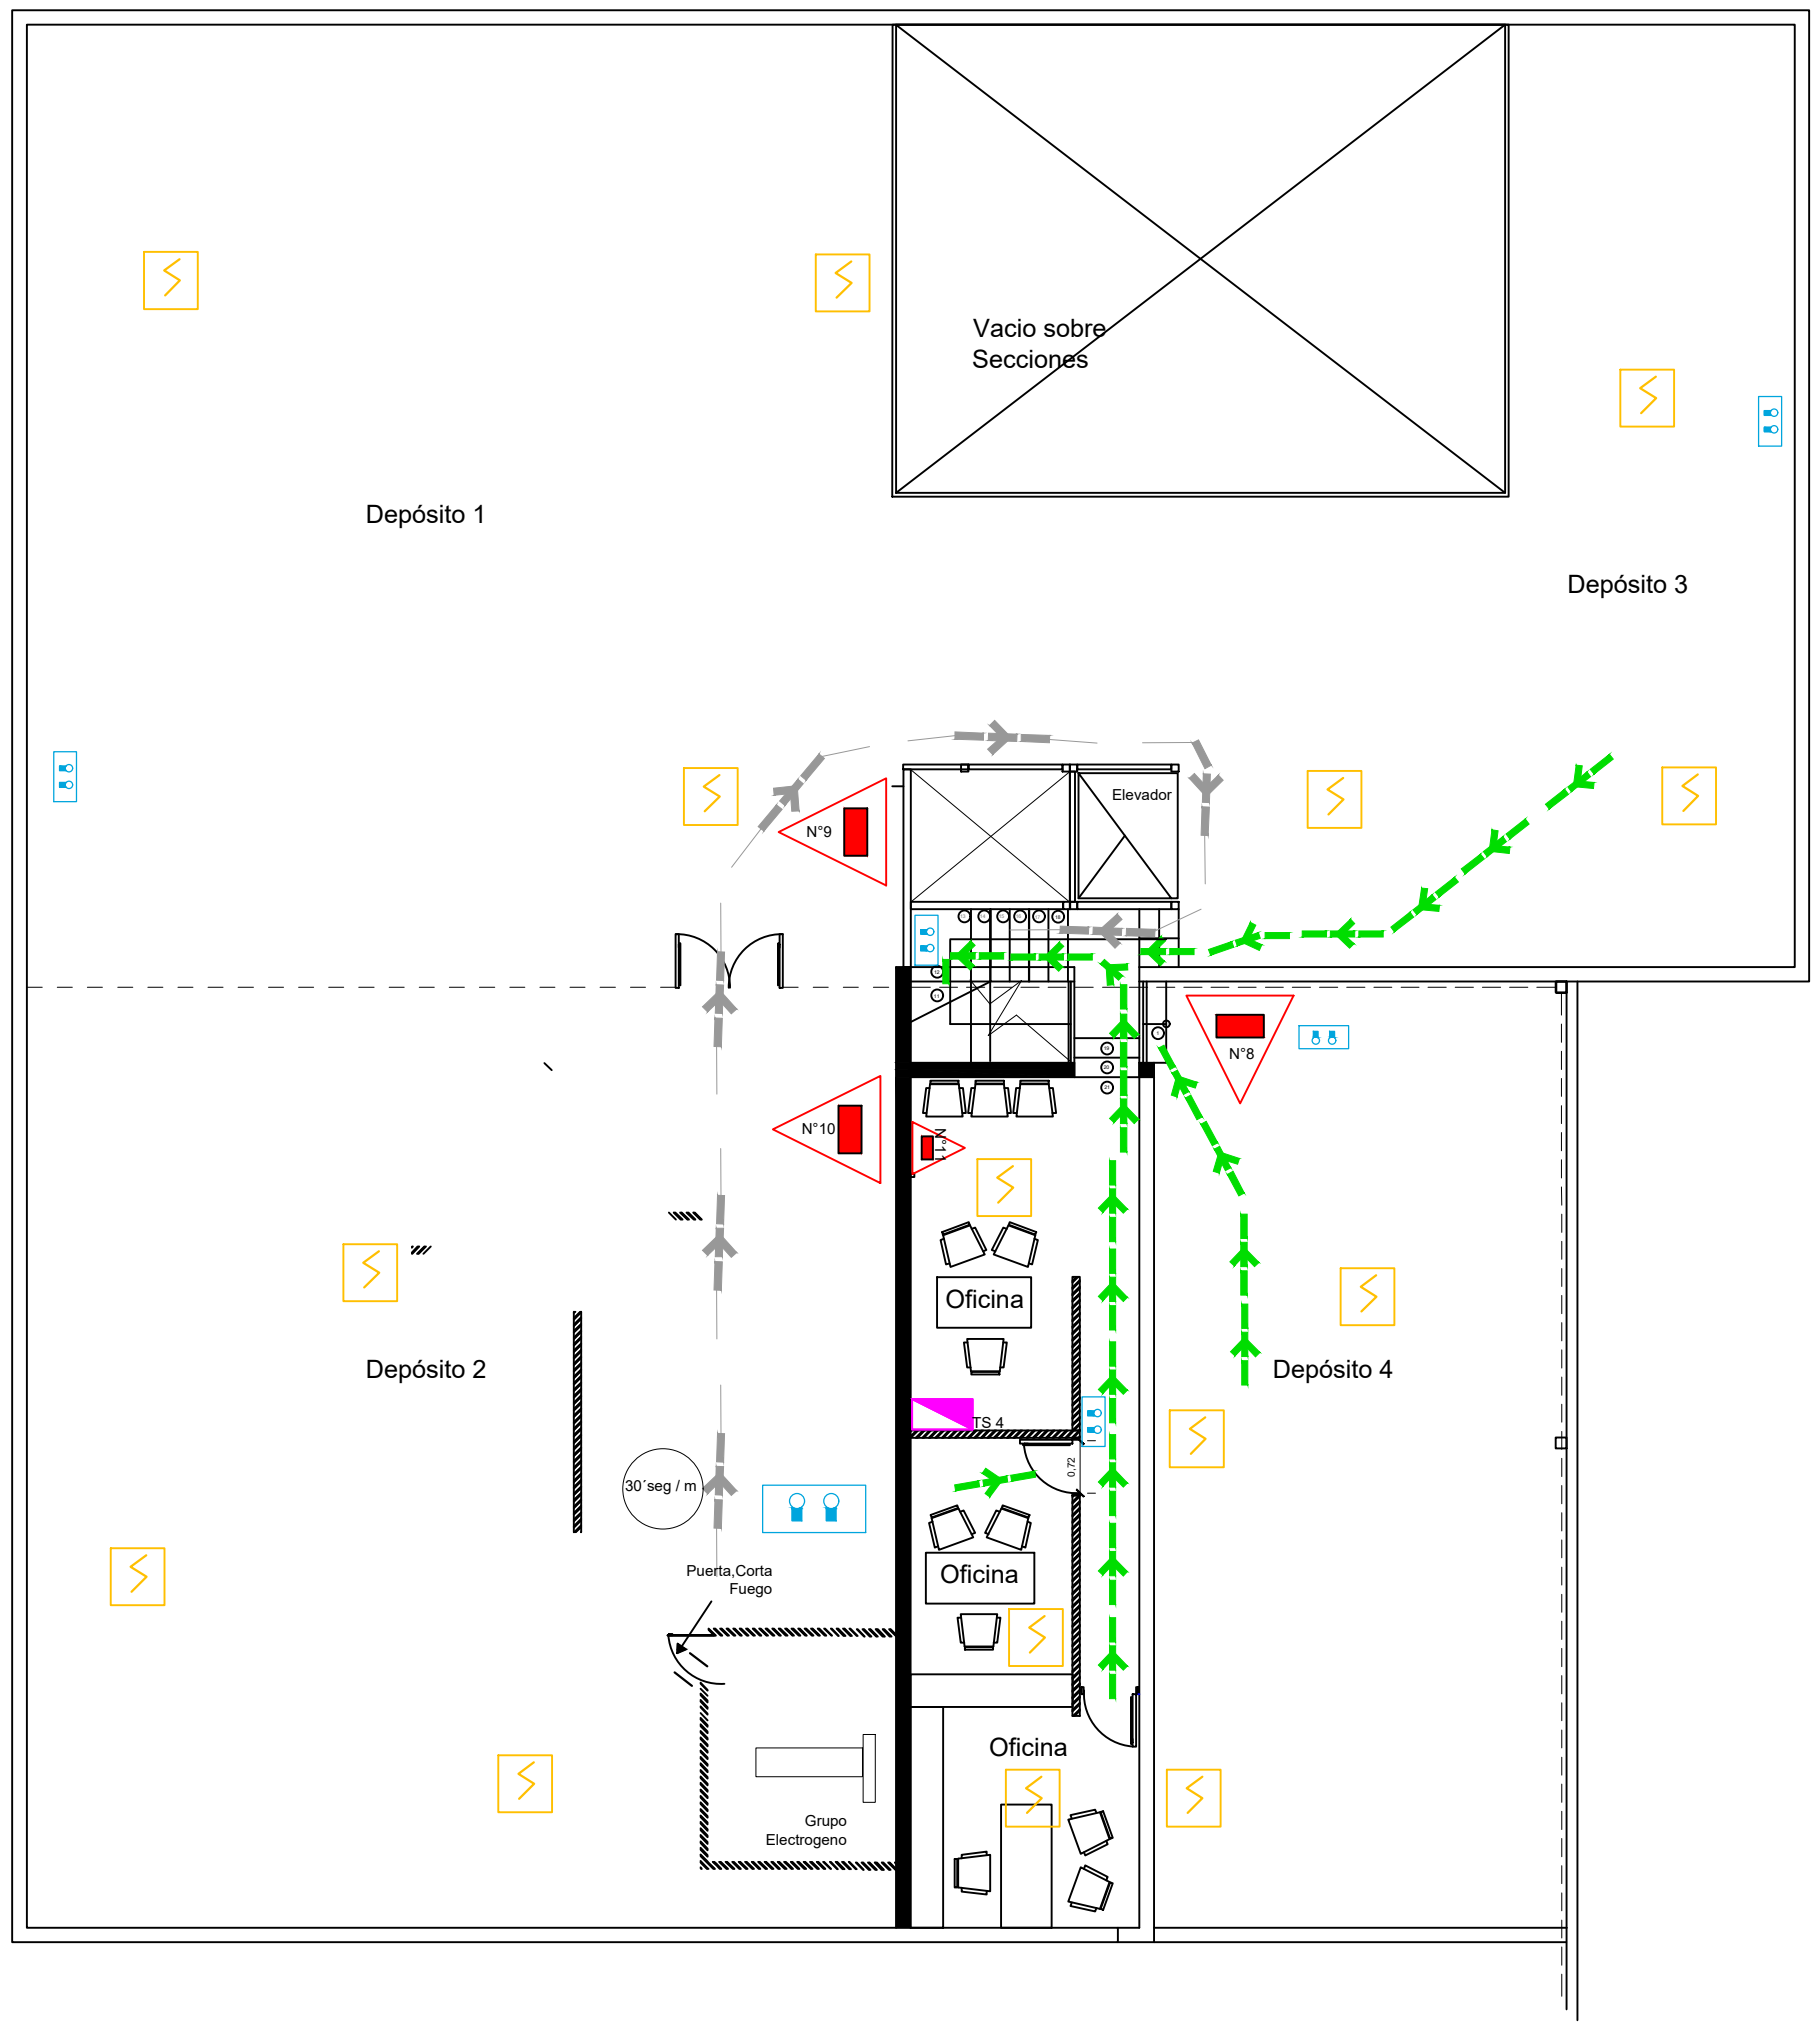

PLANTA ALTA

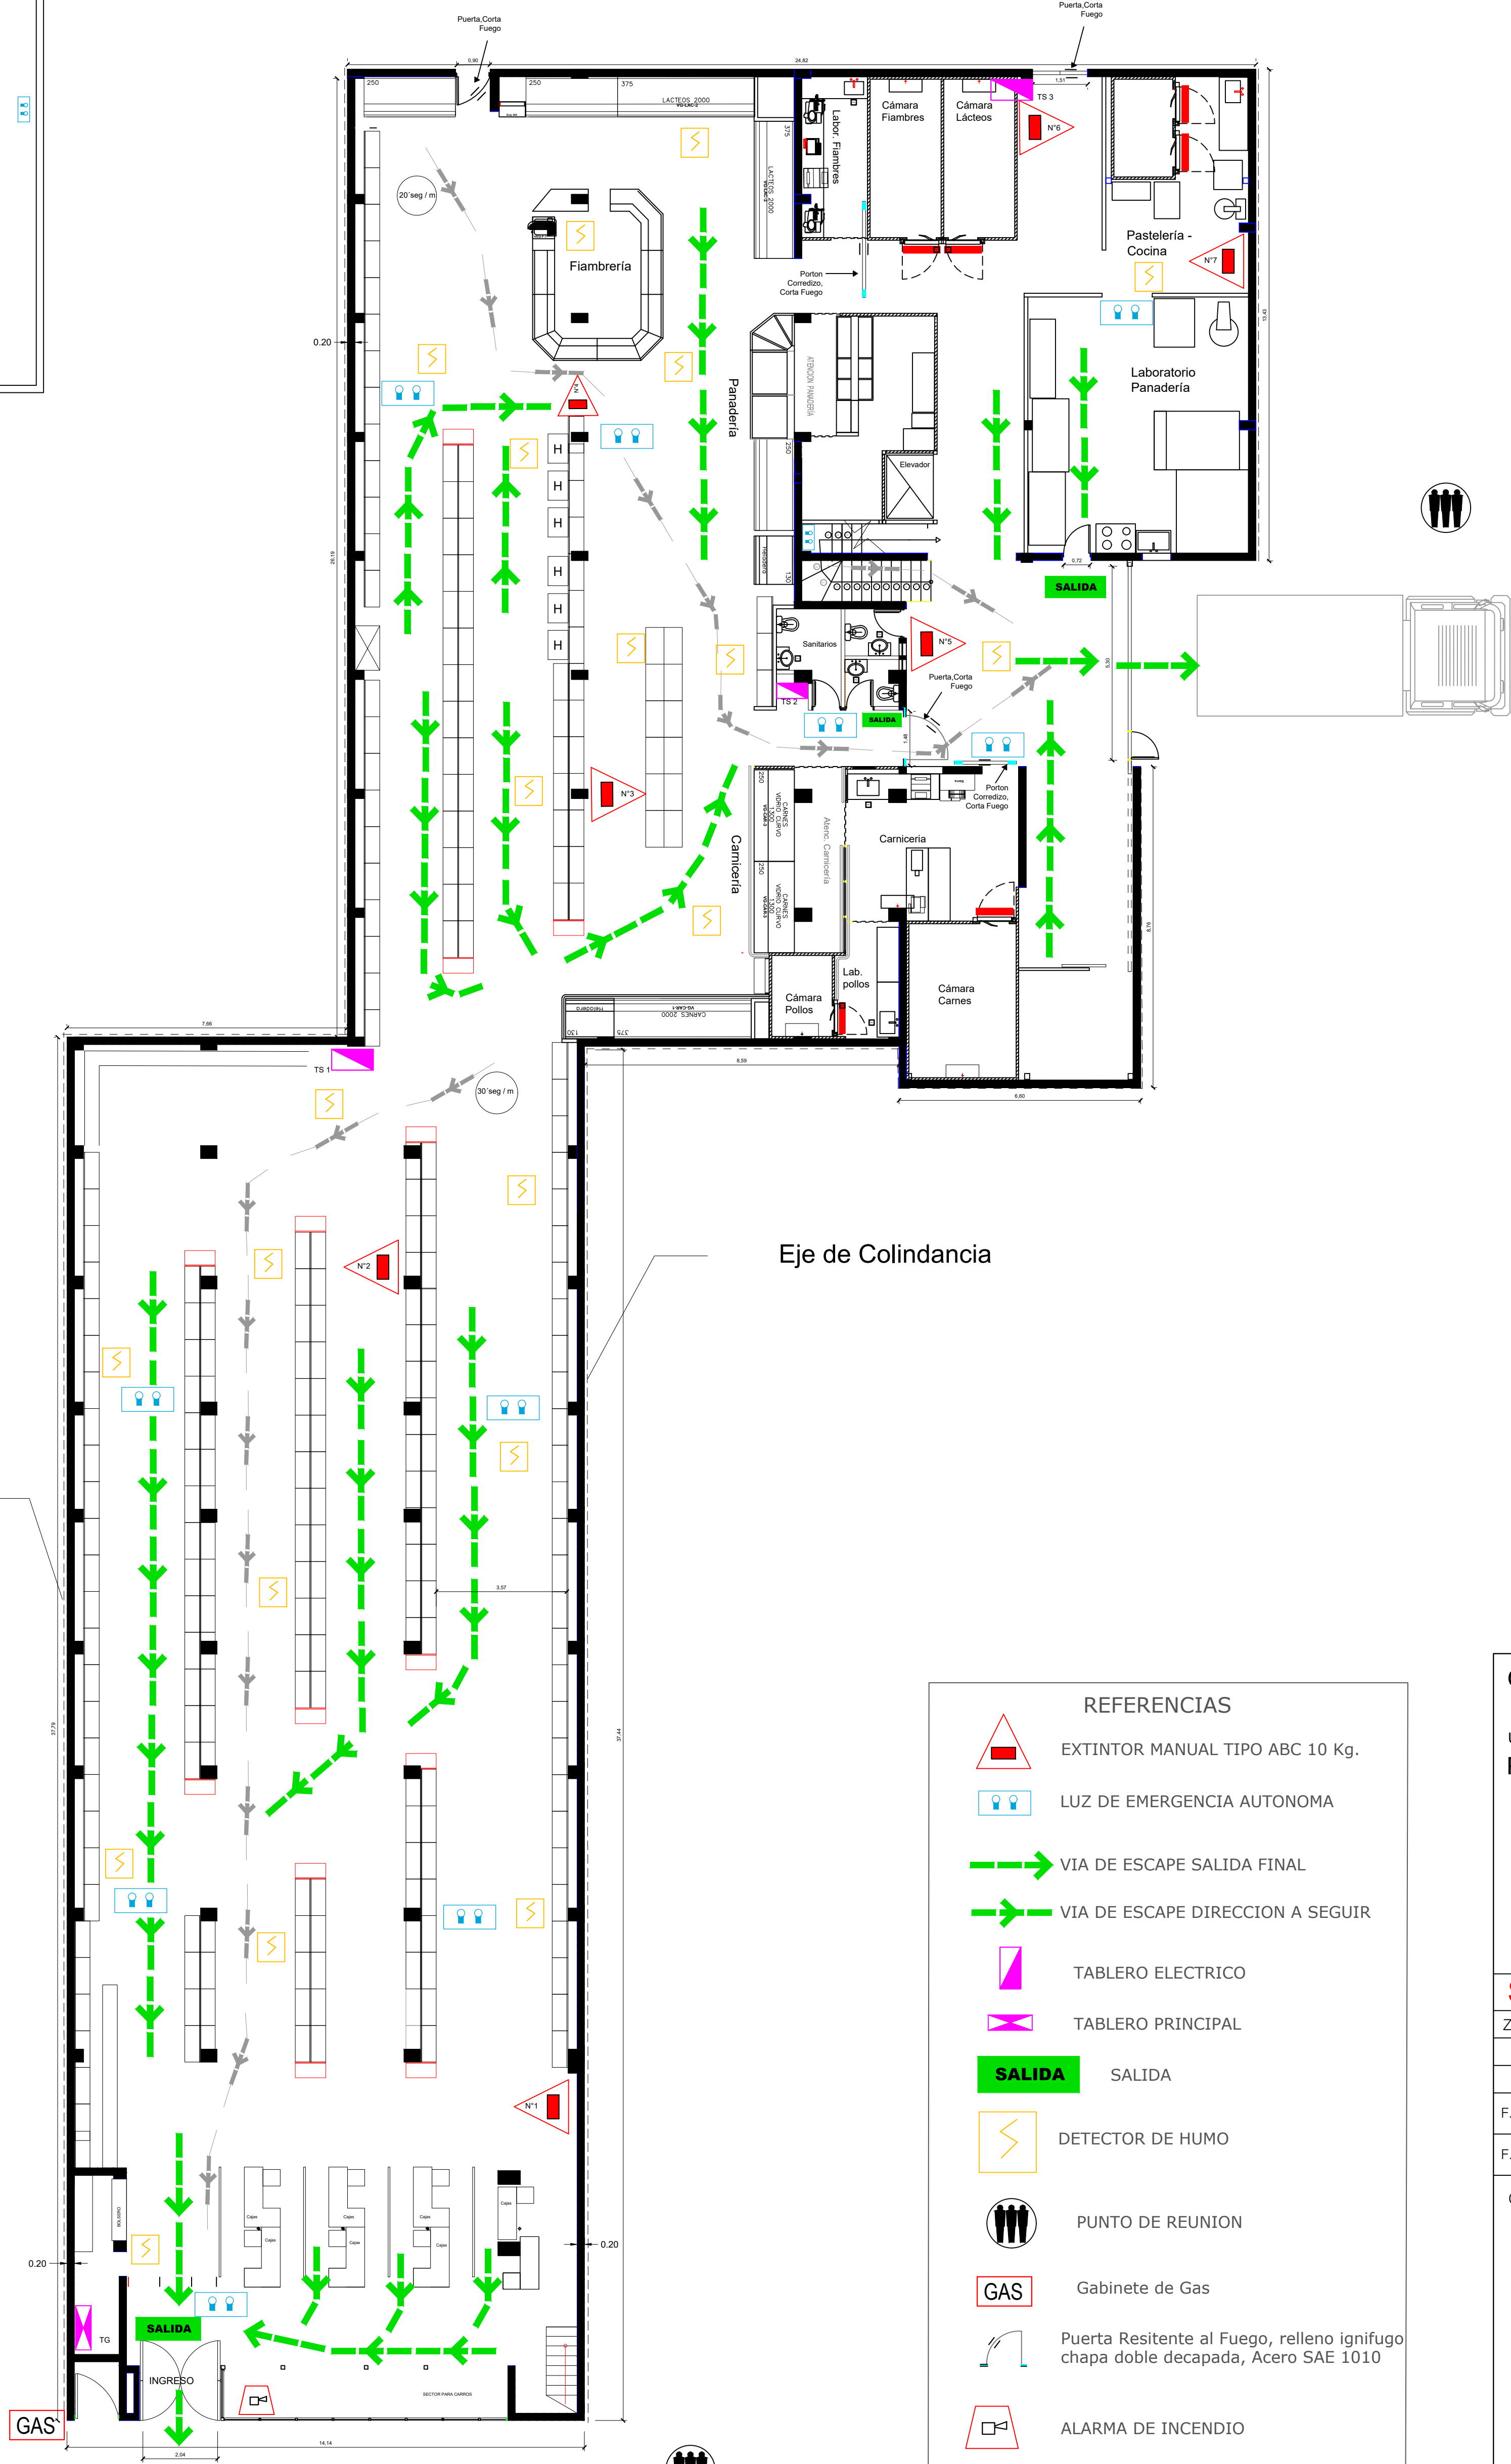

Eje de Colindancia

Eje de Colindancia

Calle Saenz Peña

Calle Patricios

REFERENCIAS

EXTINTOR MANUAL TIPO ABC 10 Kg.

LUZ DE EMERGENCIA AUTONOMA

VIA DE ESCAPE SALIDA FINAL

VIA DE ESCAPE DIRECCION A SEGUIR

TABLERO ELECTRICO

TABLERO PRINCIPAL

SALIDA

DETECTOR DE HUMO

PUNTO DE REUNION

GAS

Gabinete de Gas

ALARMA DE INCENDIO

TIEMPO DE EVACUACION  
(a la salida mas cercana)

OBRA: SISTEMA DE PROTECCION CONTRA INCENDIO  
NINO SUPERMERCADO

Ubicacion: CALLE SAENZ PEÑA 249 LUJAN DE CUYO  
PROPIETARIO: BOSIN S.A.

Sup. Salon de Venta:..... 687 m²  
Sup. Deposito planta baja:.... 259 m²  
Sup. Deposito Planta Alta:.... 523 m²  
Sup. TOTAL:..... 1671 m²

SISTEMA CONTRA INCENDIO

Esc= 1:100

ZONA:

|                |               |             |               |
|----------------|---------------|-------------|---------------|
| INDICE DE ZONA | IND. DE PROY. | P. M: 21037 | P. R:         |
| VALORES        | SUPERF. (m²)  | VALOR       | SUP. CUB (m³) |
| F.O.S. MIN     | .....         | .....       | .....         |
| F.O.S. MAX     | .....         | .....       | .....         |
| F.O.T. MIN     | .....         | .....       | .....         |
| F.O.T. MAX     | .....         | .....       | .....         |

NUMERO EXPEDIENTE MUNICIPAL:

PROYECTO DE INCENDIO:

CROQUIS DE UBICACION:

VISACION PREVIA:

VISACION OFICINA TECNICA: